

建设单位:深圳卓越南山房地产开发有限公司
CLIENT:




奥意建筑设计有限公司
A+E Design Co., Ltd.
甲级资质 A14402927
Class A Qualification, No. A14402927
建筑行业(建筑工程)甲级
Architectural Engineering Design, Class A
电子通信广电行业(电子工程)甲级
Electronic Engineering Design, Class A
网址 (URL): http://www.ae-design.cn

合作设计单位:
CODESIGN:

盖章区
STAMP AREA

1	2023.12.15	首次发行
版次	发行日期	描述
REV	ISSUE DATE	DESCRIPTION
发行记录		
工 艺	区东轩	
通信信息	赵振	
电 气	赵振	
气体动力		
暖通空调	陈日荣	
给排水	李素清	
结 构	张健	
建筑总图	黄晓东	
专 业	姓 名	签 署
DISCIPLINE	FULL NAME	SIGNATURE
会 签 COORDINATION		
项目总负责	项目类别	
PRIMARY CAPTAIN	PROJECT CATEGORY	
项目经理	陆耀耀	
PROJECT MANAGER	陆耀耀	
审 定	吴昌伟	
APPROV	吴昌伟	
审 核	赵振	
EXAMIN	赵振	
专业负责	虞 媛	
MAIN ENGINEER	虞 媛	
校 对	连一静	
CHKD	连一静	
设 计	吕文	
DESIGN	吕文	
制 图		
DRAWN		
职 务	姓 名	签 署
DUTY	FULL NAME	SIGNATURE
设 计 签 署 SIGNATURE		
设计阶段	施工图	专 业
JOB STAGE	CONSTRUCTION DRAWING	DISCIPLINE
项目名称	玻璃公馆	
PROJECT	玻璃公馆	
子项名称		
ITEM		
图 名	02户型空调配电平面图	
DWG TITLE	02户型空调配电平面图	
工程号	子项号	图 号
PROJECT NO	ITEM NO	DWG NO
22085		99-DE-D05
比 例	1	
SCALE	1	

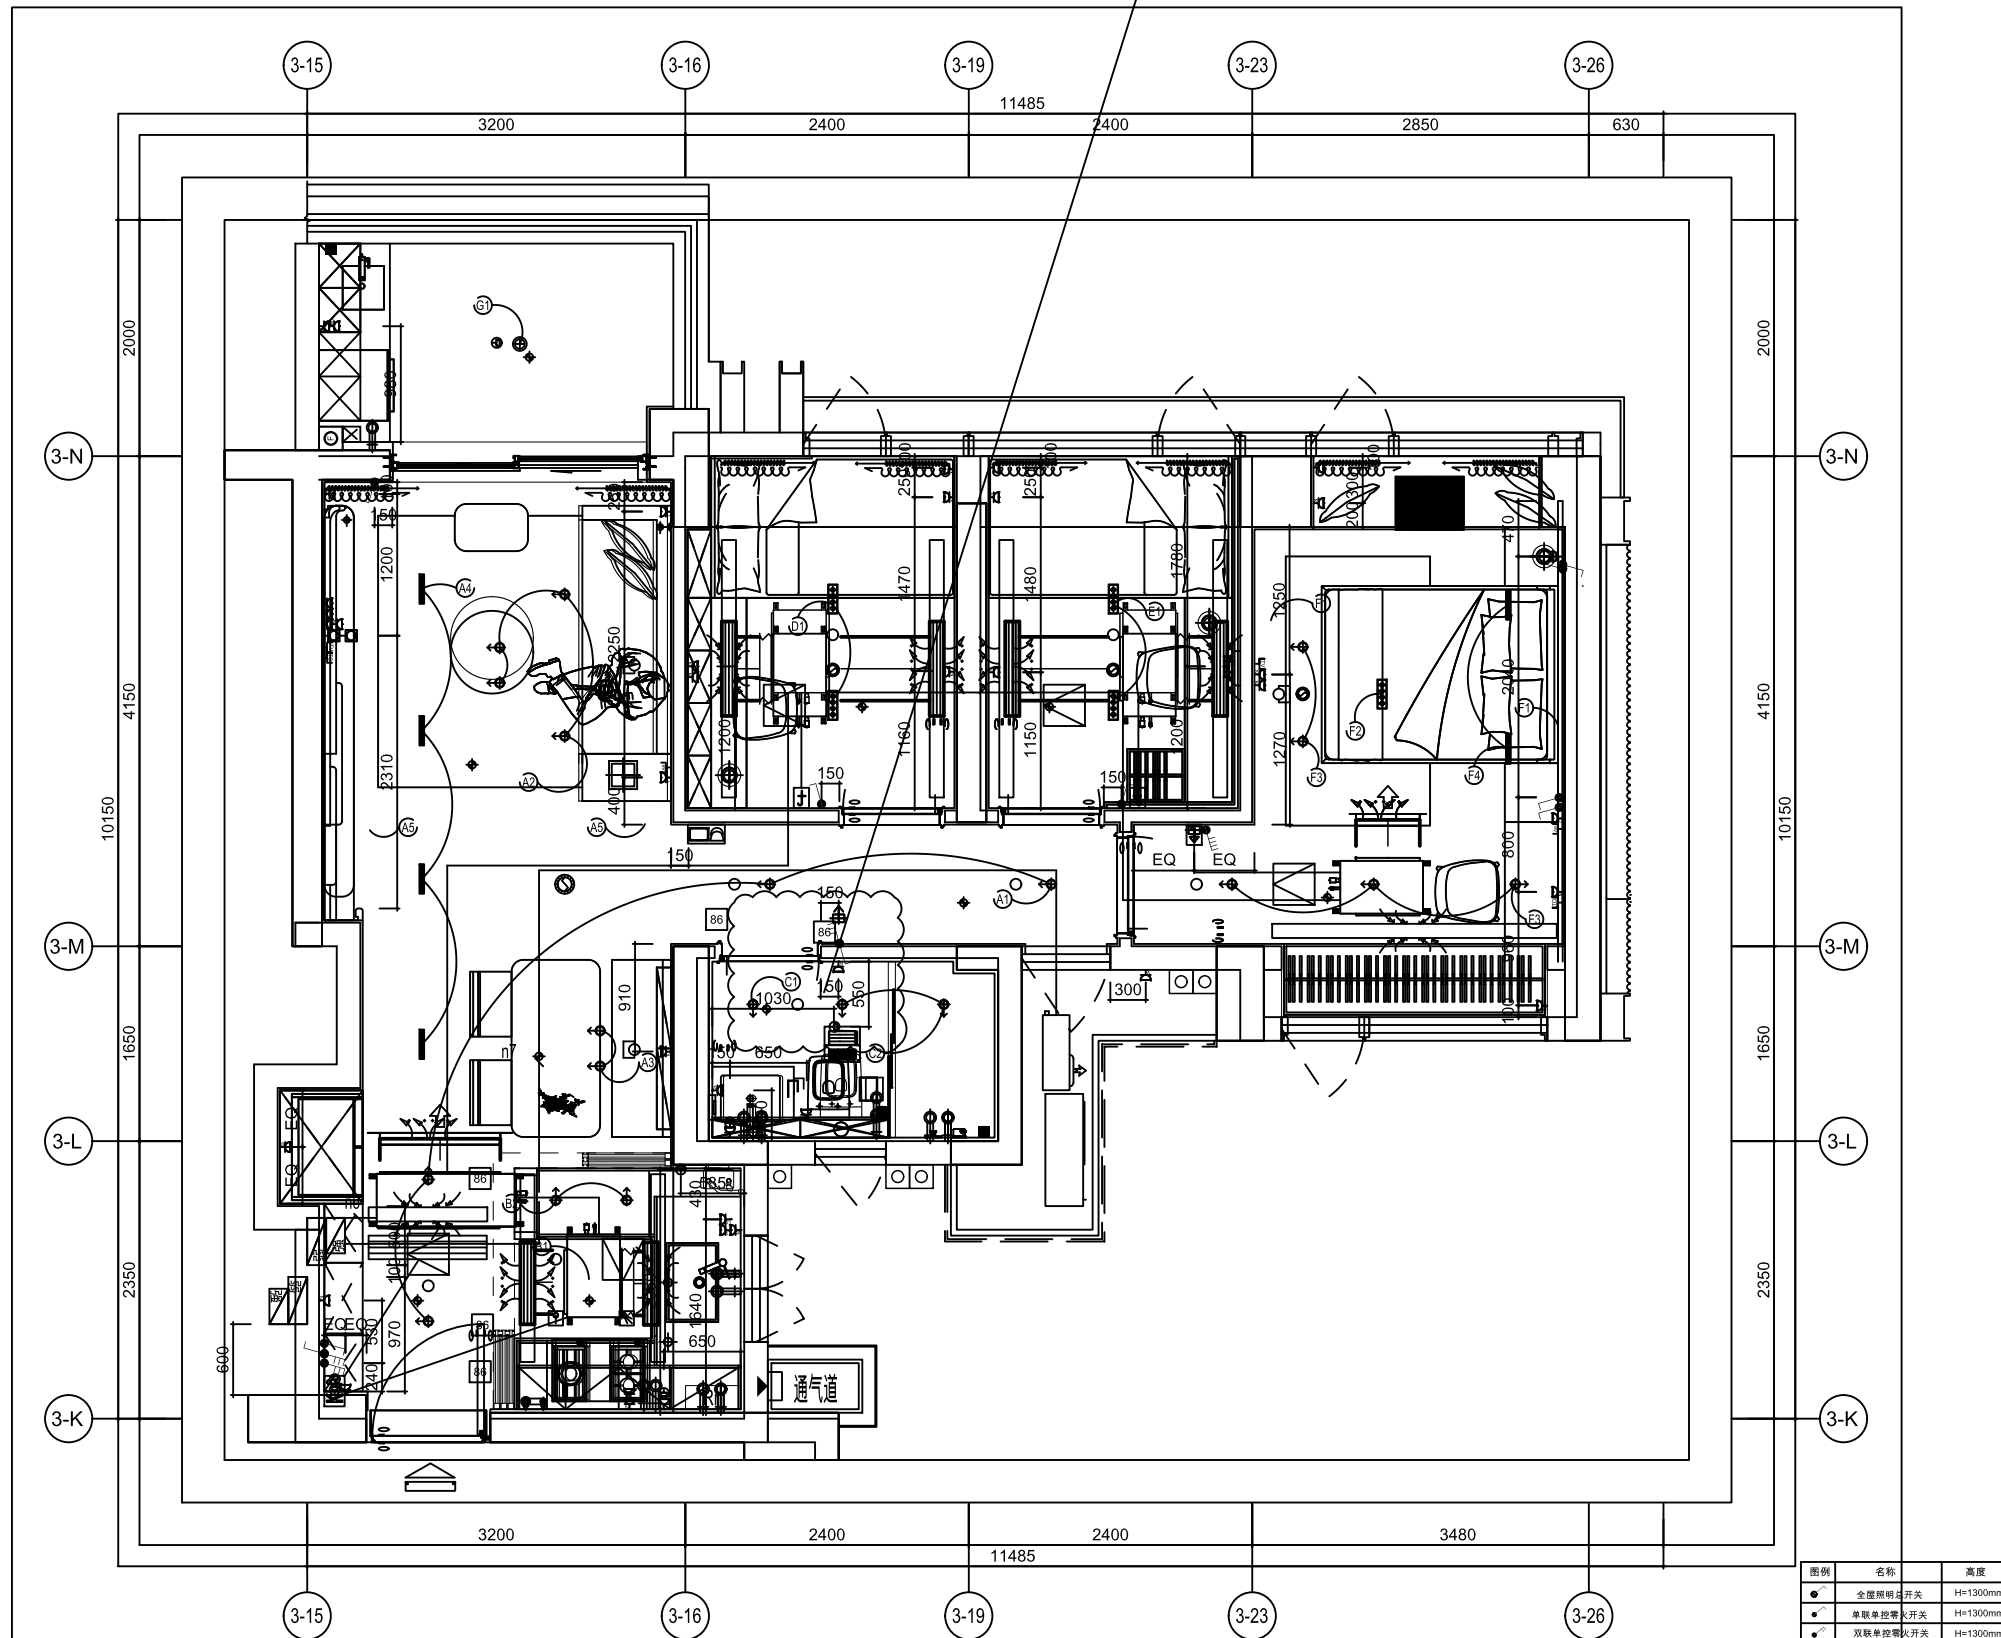

图例	名称	高度
●	全置照明开关	H=1300mm
●	单联单控开关	H=1300mm
●	双联单控开关	H=1300mm
●	三联单控开关	H=1300mm
●	单联双控开关	H=1300mm
●	双联双控开关	H=1300mm
●	三联双控开关	H=1300mm
■	空调温控开关	H=1300mm
■	新风面板	H=1300mm

说明:
空调室内机引至空调室内机开关预留: PC25-WC,CC
新风机引至新风机开关预留: WDZB-KYJY-B2-5x0.75-PC25-WC,CC
具体由厂家配套