


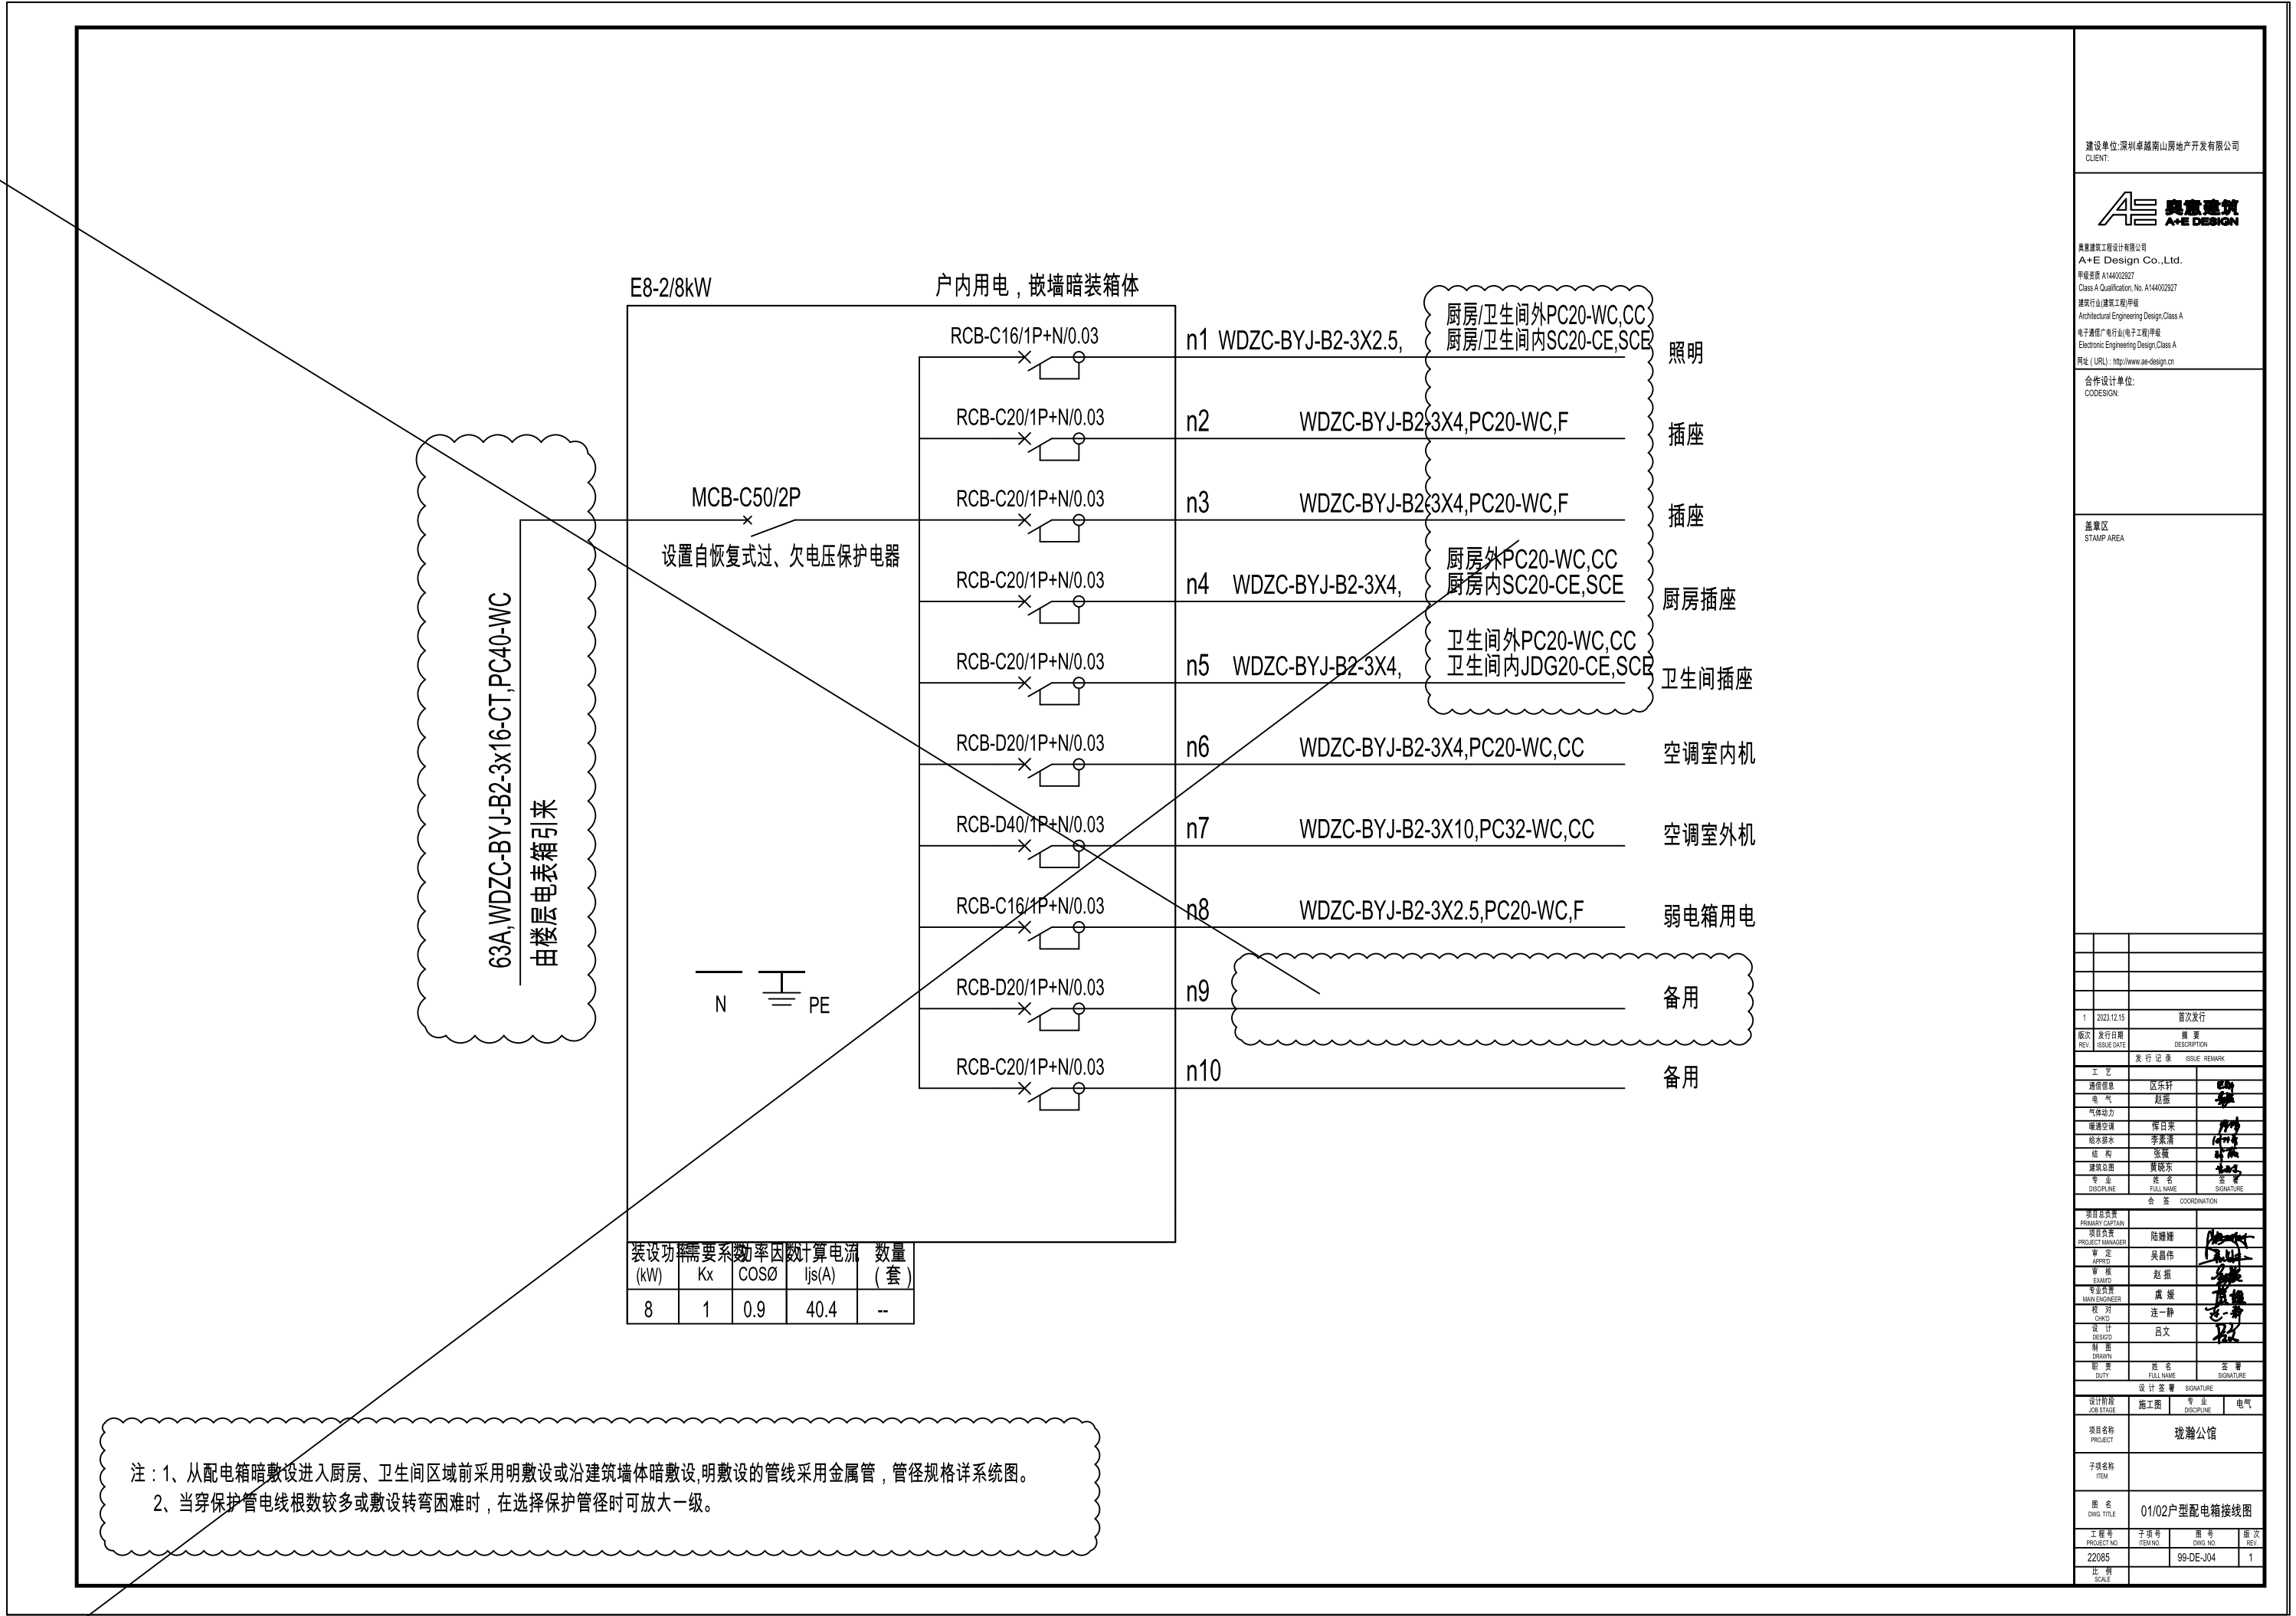

建设单位:深圳卓越南山房地产开发有限公司
CLIENT:



奥意建筑工程设计有限公司
A+E Design Co., Ltd.
甲级资质 A14402927
Class A Qualification, No. A14402927
建筑行业(建筑工程)甲级
Architectural Engineering Design, Class A
电子通信广电行业(电子工程)甲级
Electronic Engineering Design, Class A
网址 (URL): http://www.ae-design.cn

合作设计单位:
CODESIGN:

盖章区
STAMP AREA

1	2023.12.15	首次发行
版次	发行日期	描述
REV	ISSUE DATE	DESCRIPTION
发行记录		
工 艺	区东轩	
通 信	赵振	
电 气	赵振	
气 体 动 力		
暖通空调	陈日荣	
给排水	李素清	
结 构	张健	
建筑总图	黄晓东	
专 业	姓 名	签 署
DISCIPLINE	FULL NAME	SIGNATURE
会 签		
项目总负责		
PRIMARY CAPTAIN		
项目经理	陆耀耀	
PROJECT MANAGER		
审 定	吴昌伟	
APPROV		
审 核	赵振	
EXAMIN		
专业负责人	虞 媛	
MAIN ENGINEER		
校 对	连一静	
CHKD		
设 计	吕文	
DESIGN		
制 图		
DRAWN		
职 责	姓 名	签 署
DUTY	FULL NAME	SIGNATURE
设 计 签 署		
设计阶段	施工图	专 业
JOB STAGE	DISCIPLINE	电 气
项目名称	玻璃公馆	
PROJECT		
子项名称		
ITEM		
图 名	01/02户型配电箱接线图	
DWG TITLE		
工程号	子项号	图 号
PROJECT NO	ITEM NO	DWG NO
22085		99-DE-J04
比 例		
SCALE		
		版 次
		REV
		1