


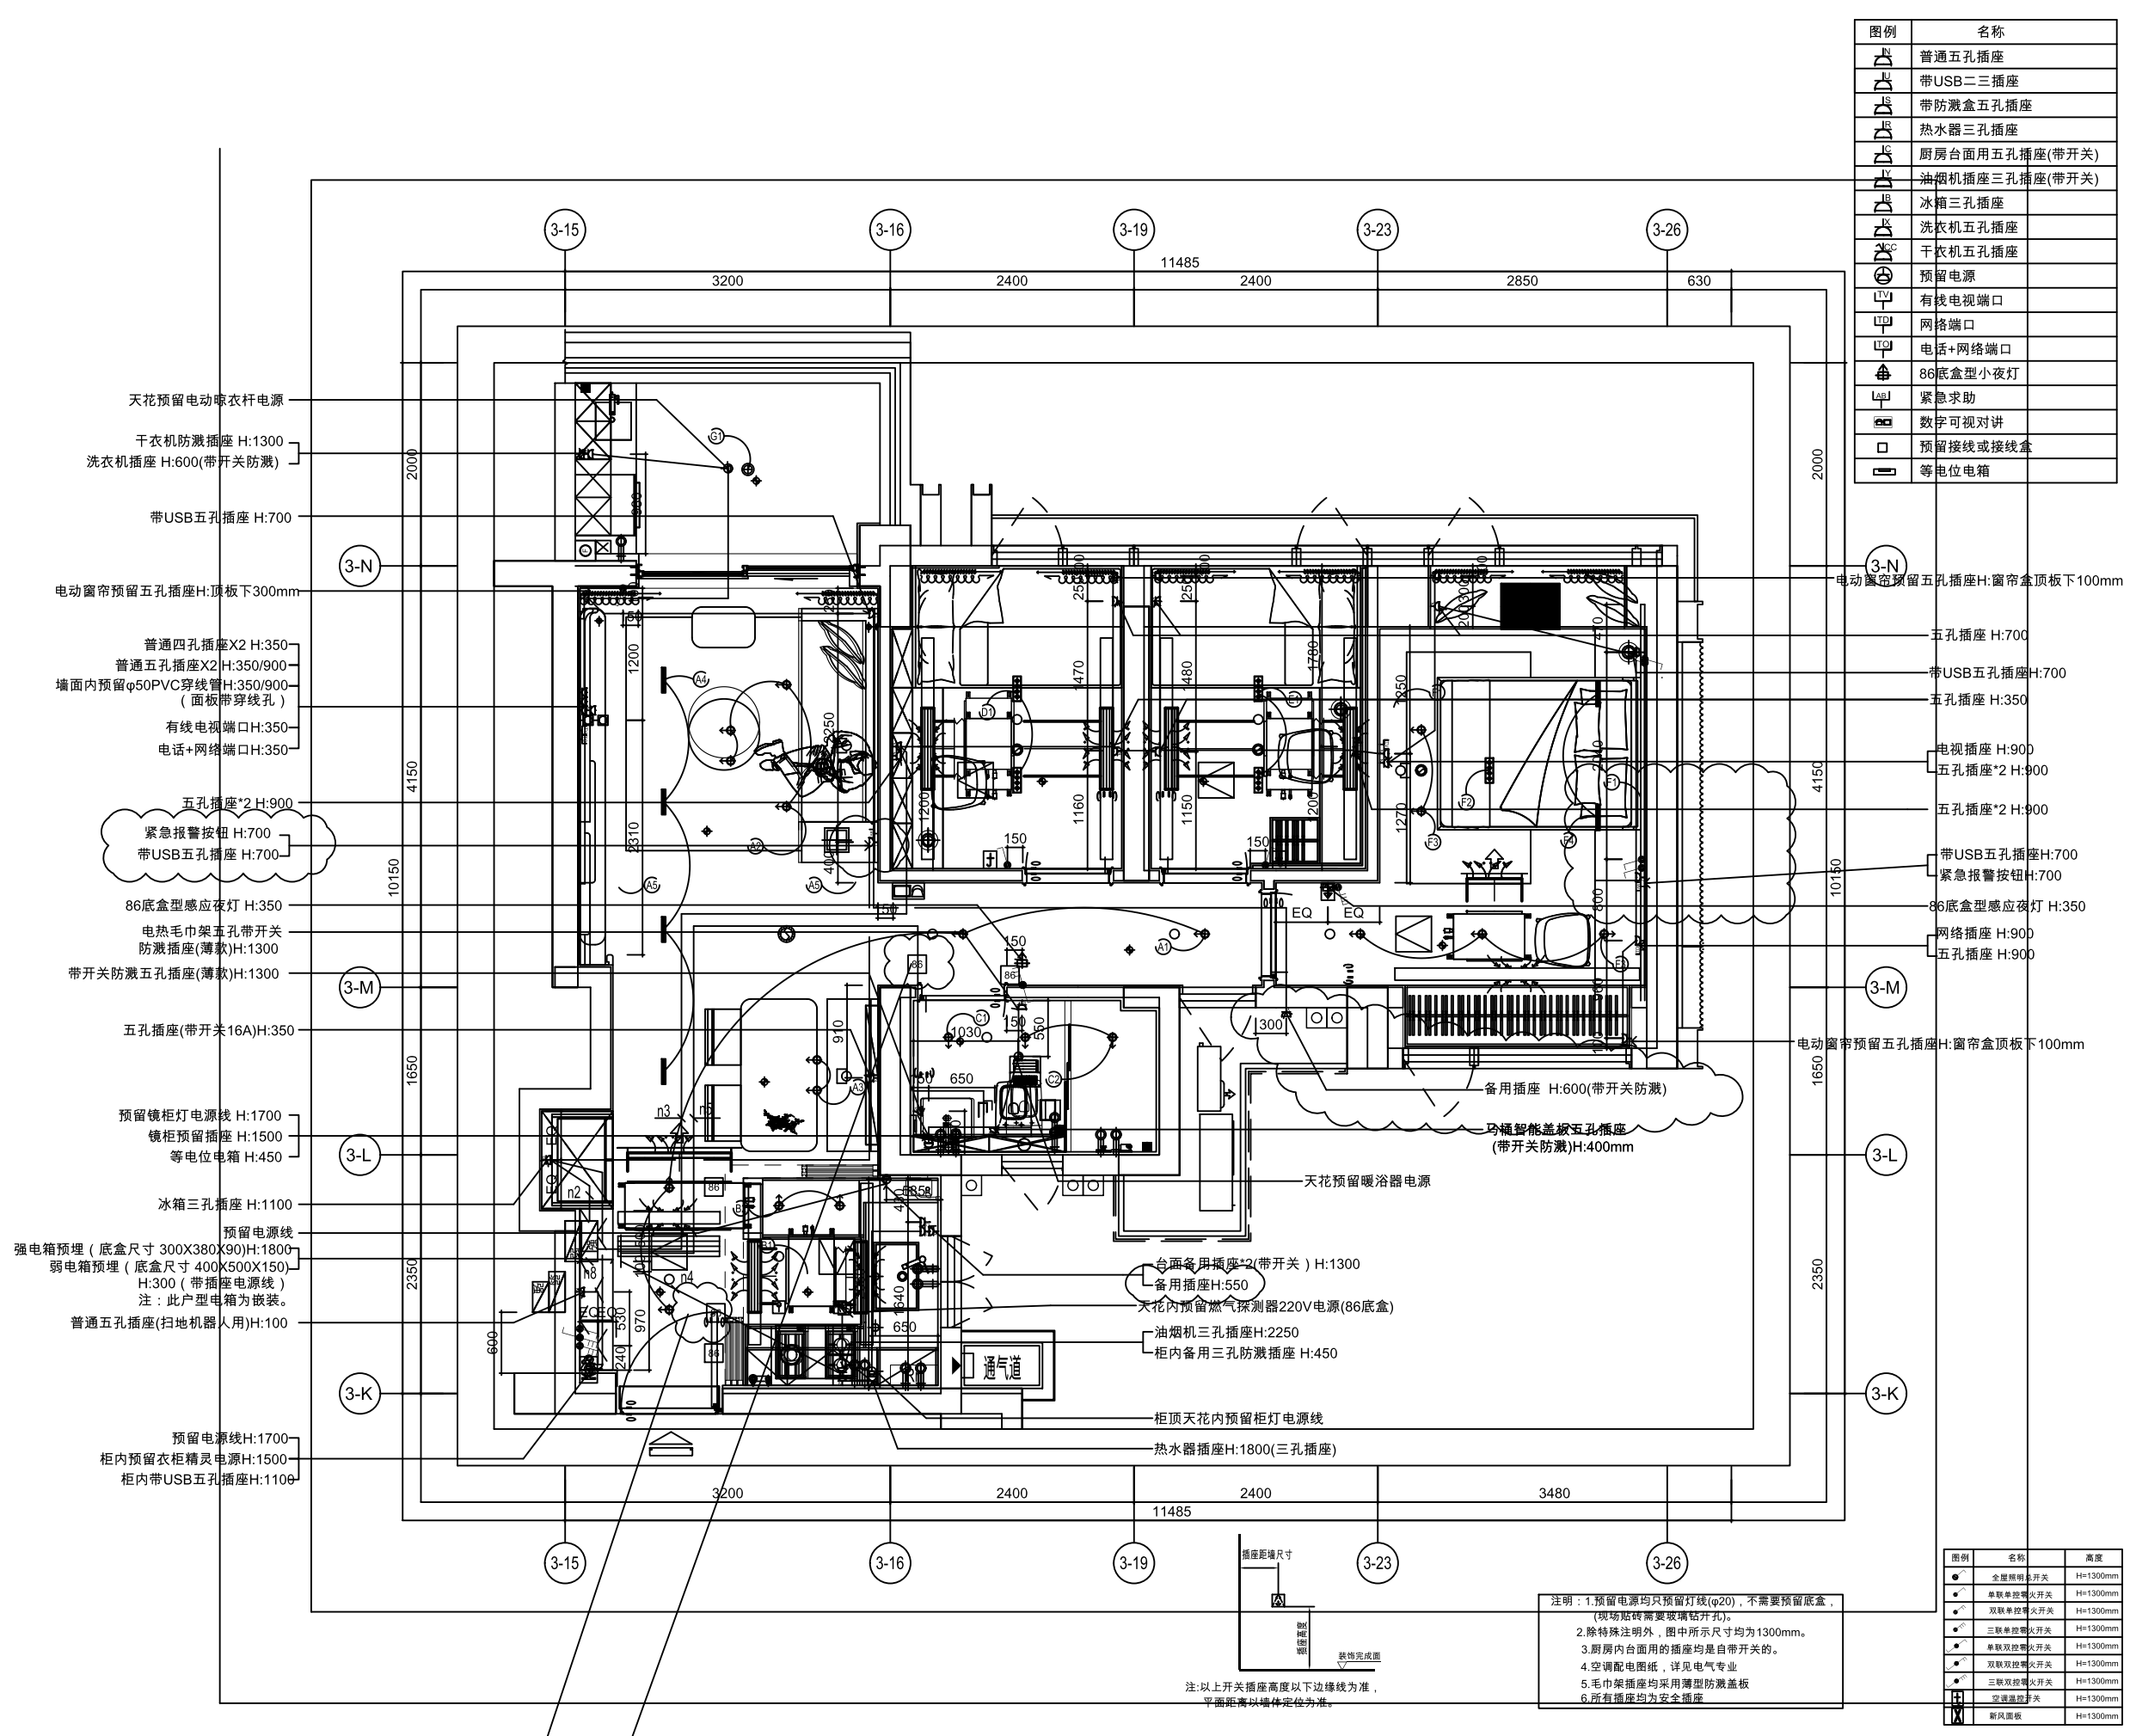

图例	名称
	普通五孔插座
	带USB二三插座
	带防溅盒五孔插座
	热水器三孔插座
	厨房台面用五孔插座(带开关)
	油烟机插座三孔插座(带开关)
	冰箱三孔插座
	洗衣机五孔插座
	干衣机五孔插座
	预留电源
	有线电视端口
	网络端口
	电话+网络端口
	86底盒型小夜灯
	紧急求助
	数字可视对讲
	预留接线或接线盒
	等电位电箱

建设单位:深圳卓越南山房地产开发有限公司
CLIENT:



奥意建筑设计有限公司
A+E Design Co., Ltd.
身份证号: A144022927
Class A Qualification, No. A144022927
建筑行业(建筑工程)甲级
Architectural Engineering Design, Class A
电子通信广电行业(电子工程)甲级
Electronic Engineering Design, Class A
网址 (URL): http://www.ae-design.cn

合作设计单位:
CODESIGN:

盖章区
STAMP AREA

1	2023.12.15	首次发行
版次	发行日期	描述
REV	ISSUE DATE	DESCRIPTION
发行记录		
工 艺	区东轩	
通信信息	赵振	
电 气	赵振	
气体动力		
暖通空调	陈日荣	
给排水	李素清	
结 构	张健	
建筑总图	黄晓东	
专 业	姓 名	签 署
DISCIPLINE	FULL NAME	SIGNATURE
会 签 COORDINATION		
项目负责	项目负责	
PRIMARY/LEADER	PROJECT MANAGER	
审 定	吴昌伟	
APPROV	赵振	
审 核	赵振	
EXAMIN	虞 媛	
专业负责	虞 媛	
MAIN ENGINEER	连一静	
校 对	吕文	
CHKD	DESIGN	
设 计	吕文	
DESIGN		
制 图		
DRAWN		
设 计		
DISCIPLINE		
设计阶段	施工图	专业
JOB STAGE	DISCIPLINE	电气
项目名称	玻璃公馆	
PROJECT		
子项名称		
ITEM		
图 名	02户型插座平面图	
DWG TITLE		
工程号	子项号	图 号
PROJECT NO.	ITEM NO.	DWG NO.
22085		99-DE-006
比 例		
SCALE		

图例	名称	高度
	全屋照明开关	H=1300mm
	单联单控开关	H=1300mm
	双联单控开关	H=1300mm
	三联单控开关	H=1300mm
	单联双控开关	H=1300mm
	双联双控开关	H=1300mm
	三联双控开关	H=1300mm
	全屋照明开关	H=1300mm

注明: 1. 预留电源均只预留灯线(φ20), 不需要预留底盒。
(现场贴砖需要玻璃钻孔开孔)。
2. 除特殊注明外, 图中所示尺寸均为1300mm。
3. 厨房内台面用的插座均是自带开关的。
4. 空调配电图纸, 详见电气专业
5. 毛巾架插座均采用薄型防溅盖板
6. 所有插座均为安全插座

注: 以上开关插座高度以下边线为准,
平面距离以墙体定位为准。